


110 kV grid
5000 MVA, R/X 0.1

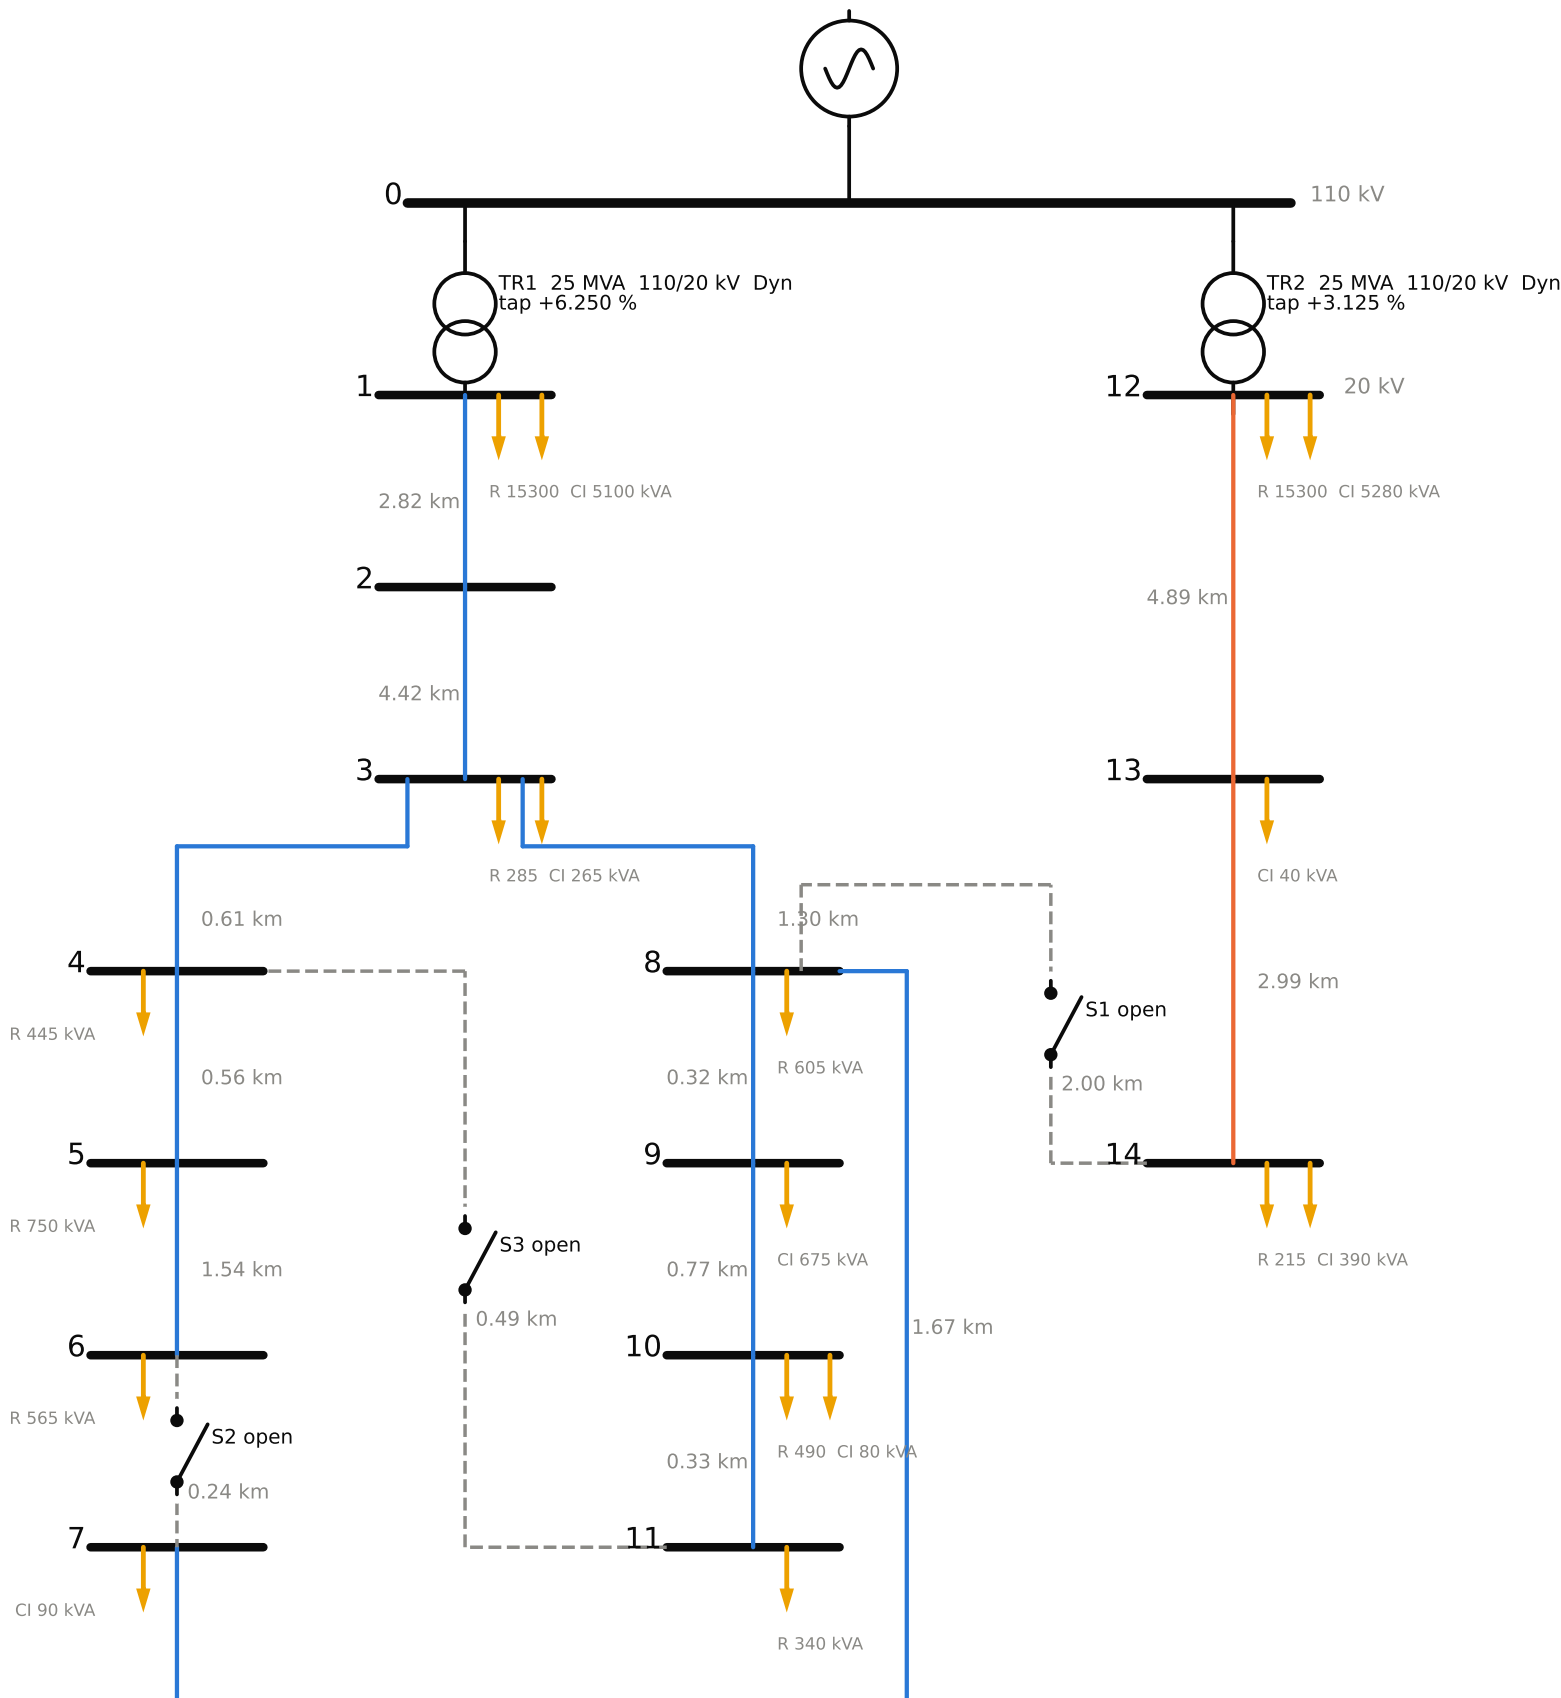

cable NA2XS2Y 120 mm², feeder 1

overhead A1 63 mm², feeder 2

tie line with switch, open in base case

load (R residential, CI commercial/industrial)